

Nyt enfamiliehus med metalindlæg i hele gulvet

Figur 1

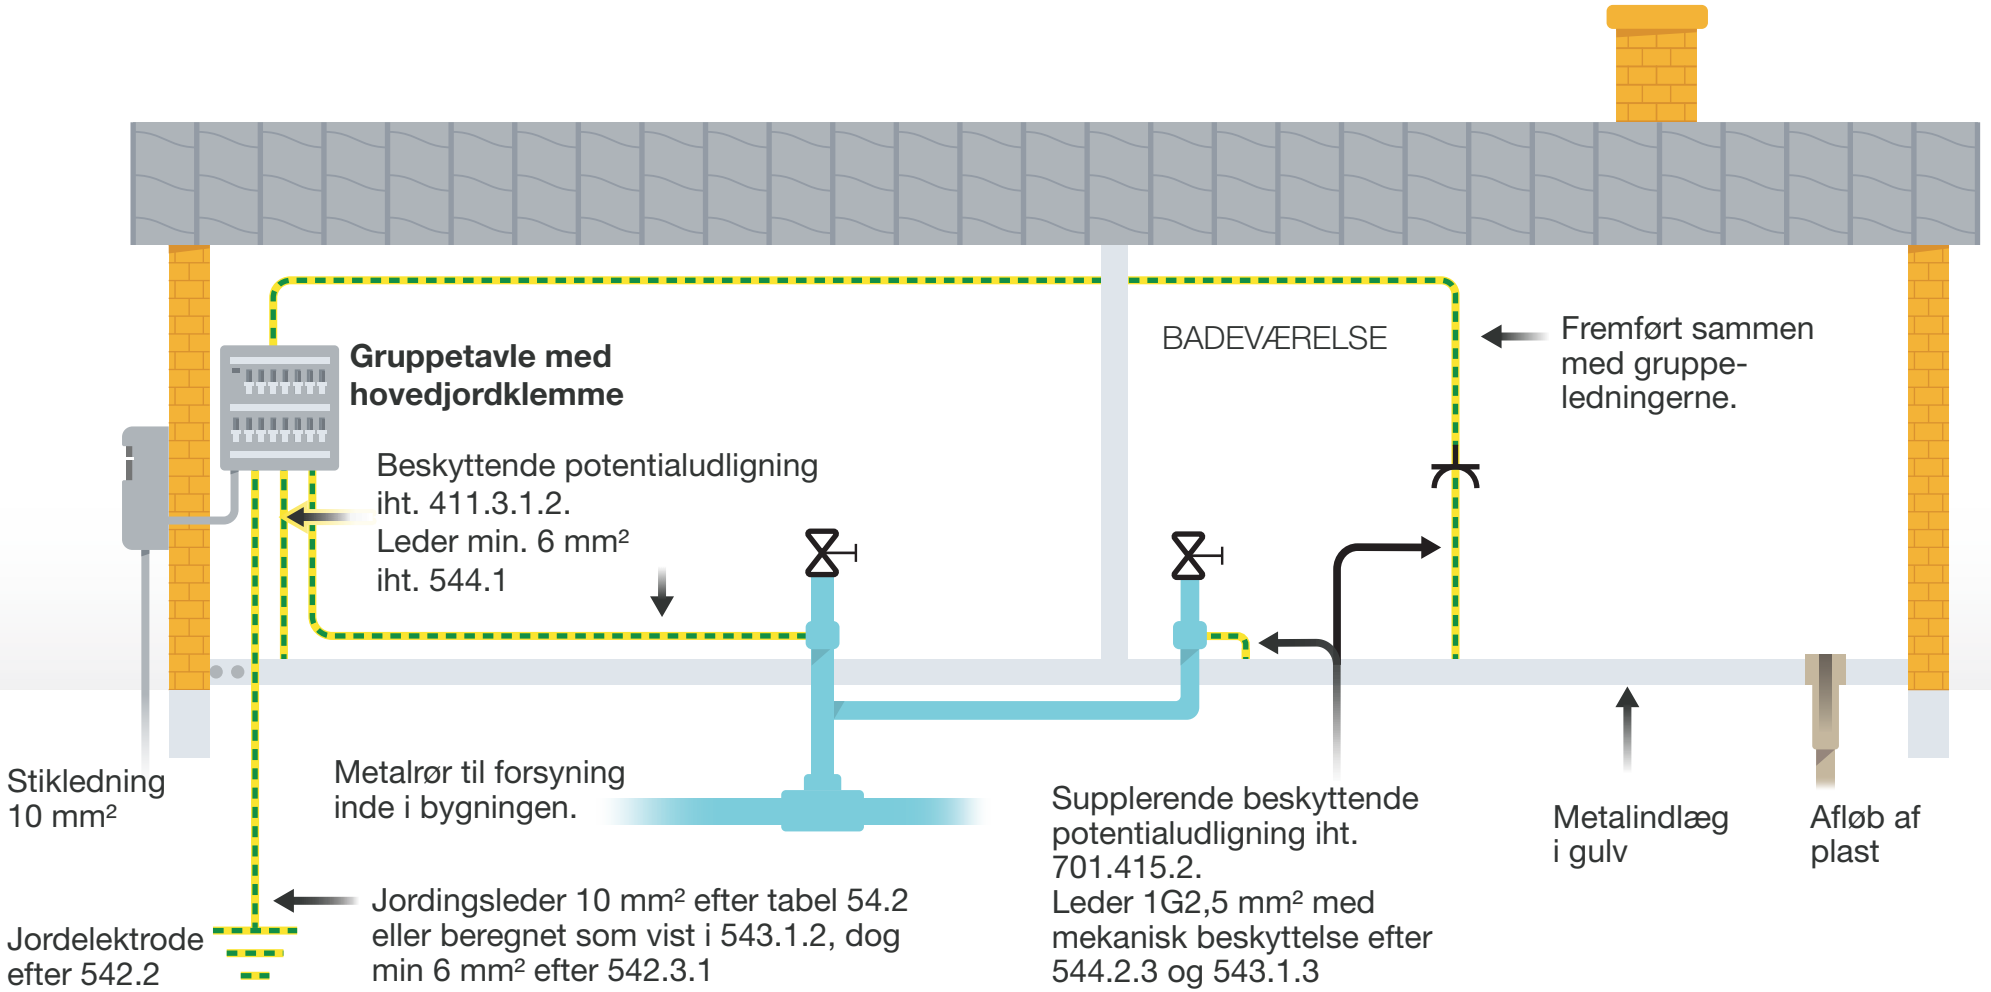


Nyt enfamiliehus anno 2017

Figur 2

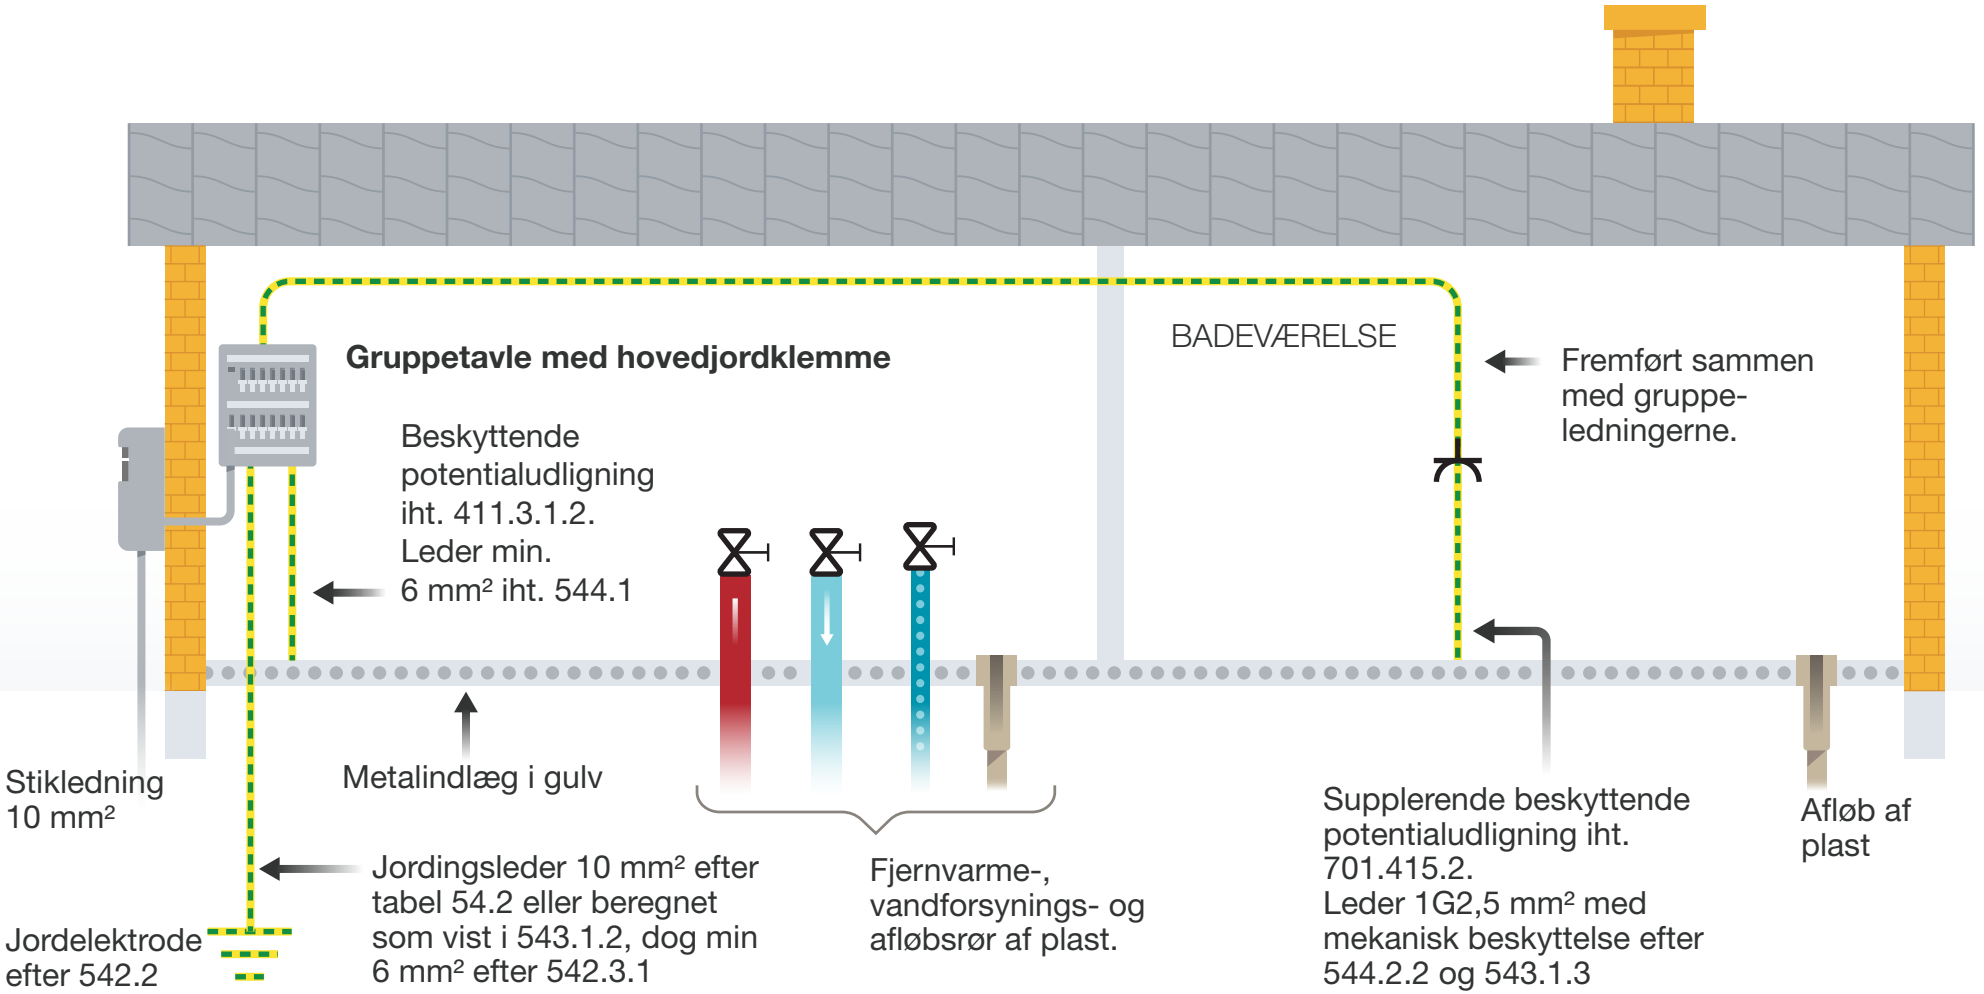


Nyt enfamiliehus hvor der kun er metalindlæg i gulvet i badeværelset

Figur 3

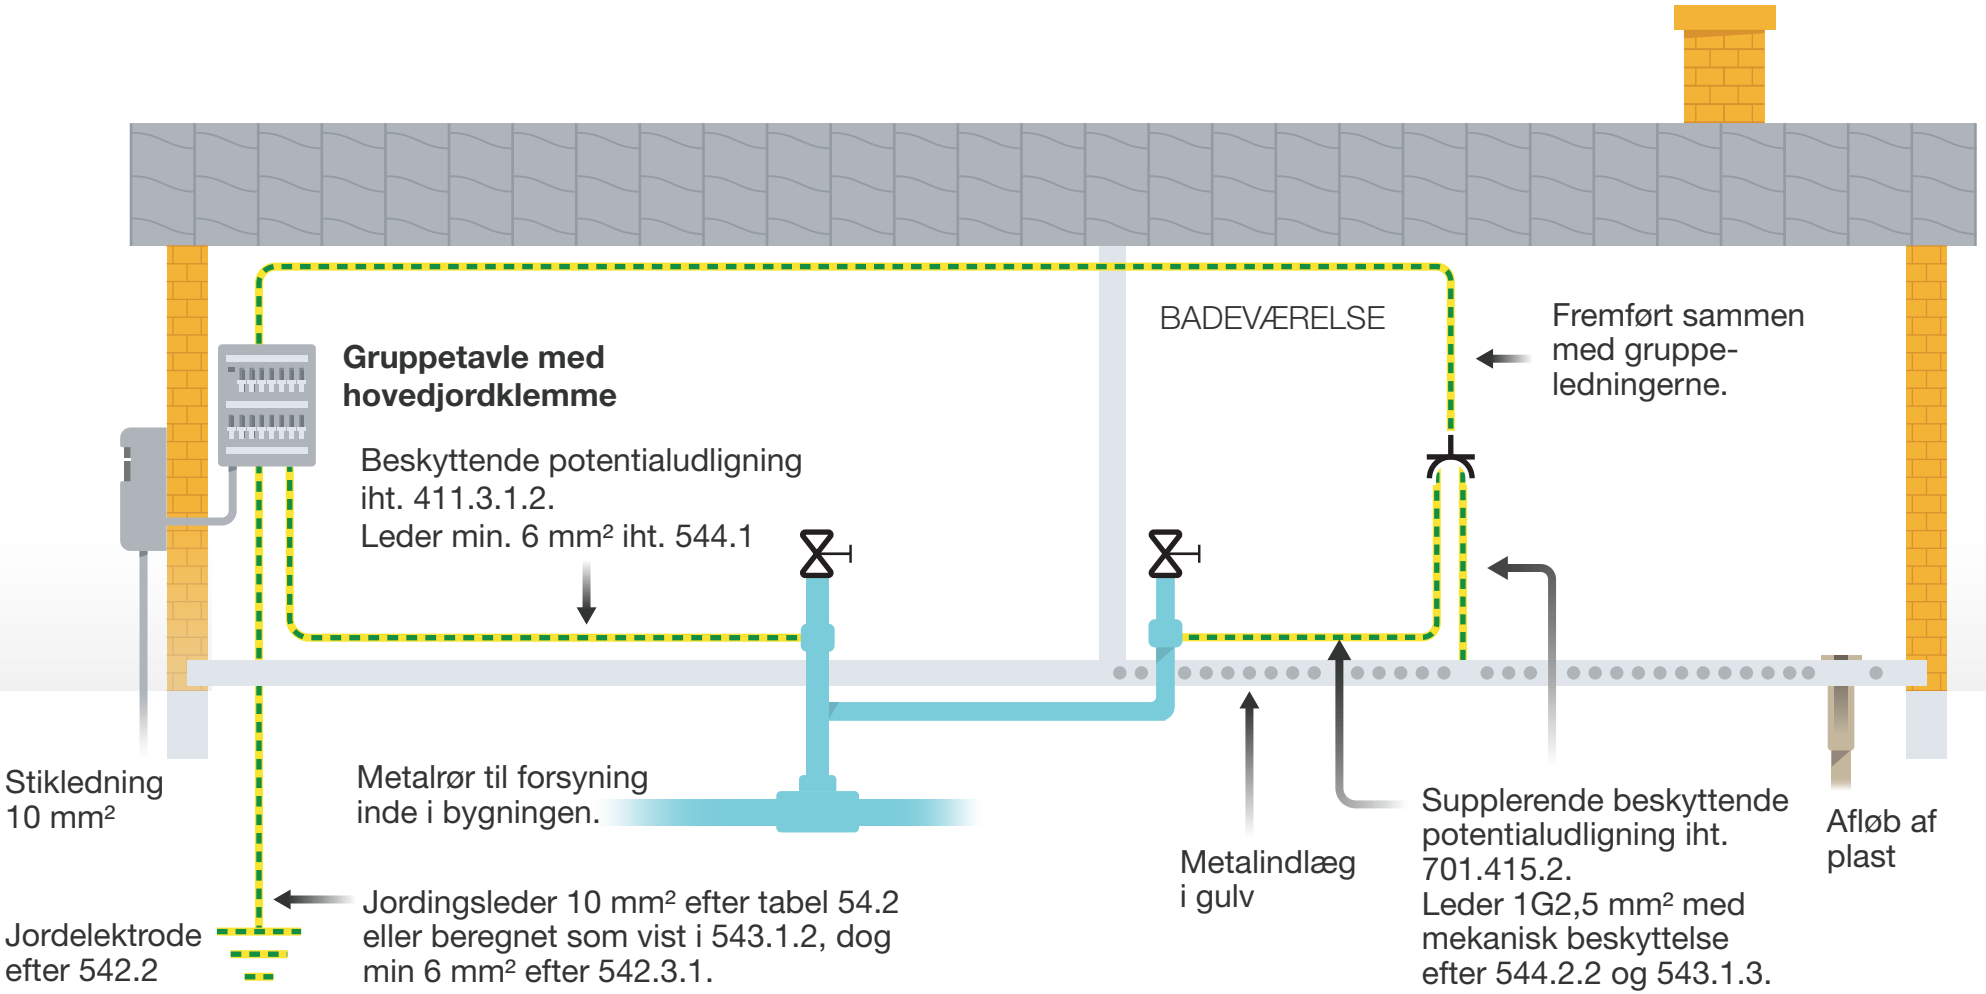


Nyt enfamiliehus med to beskyttelsesledere fremfør til badeværelset

Figur 4

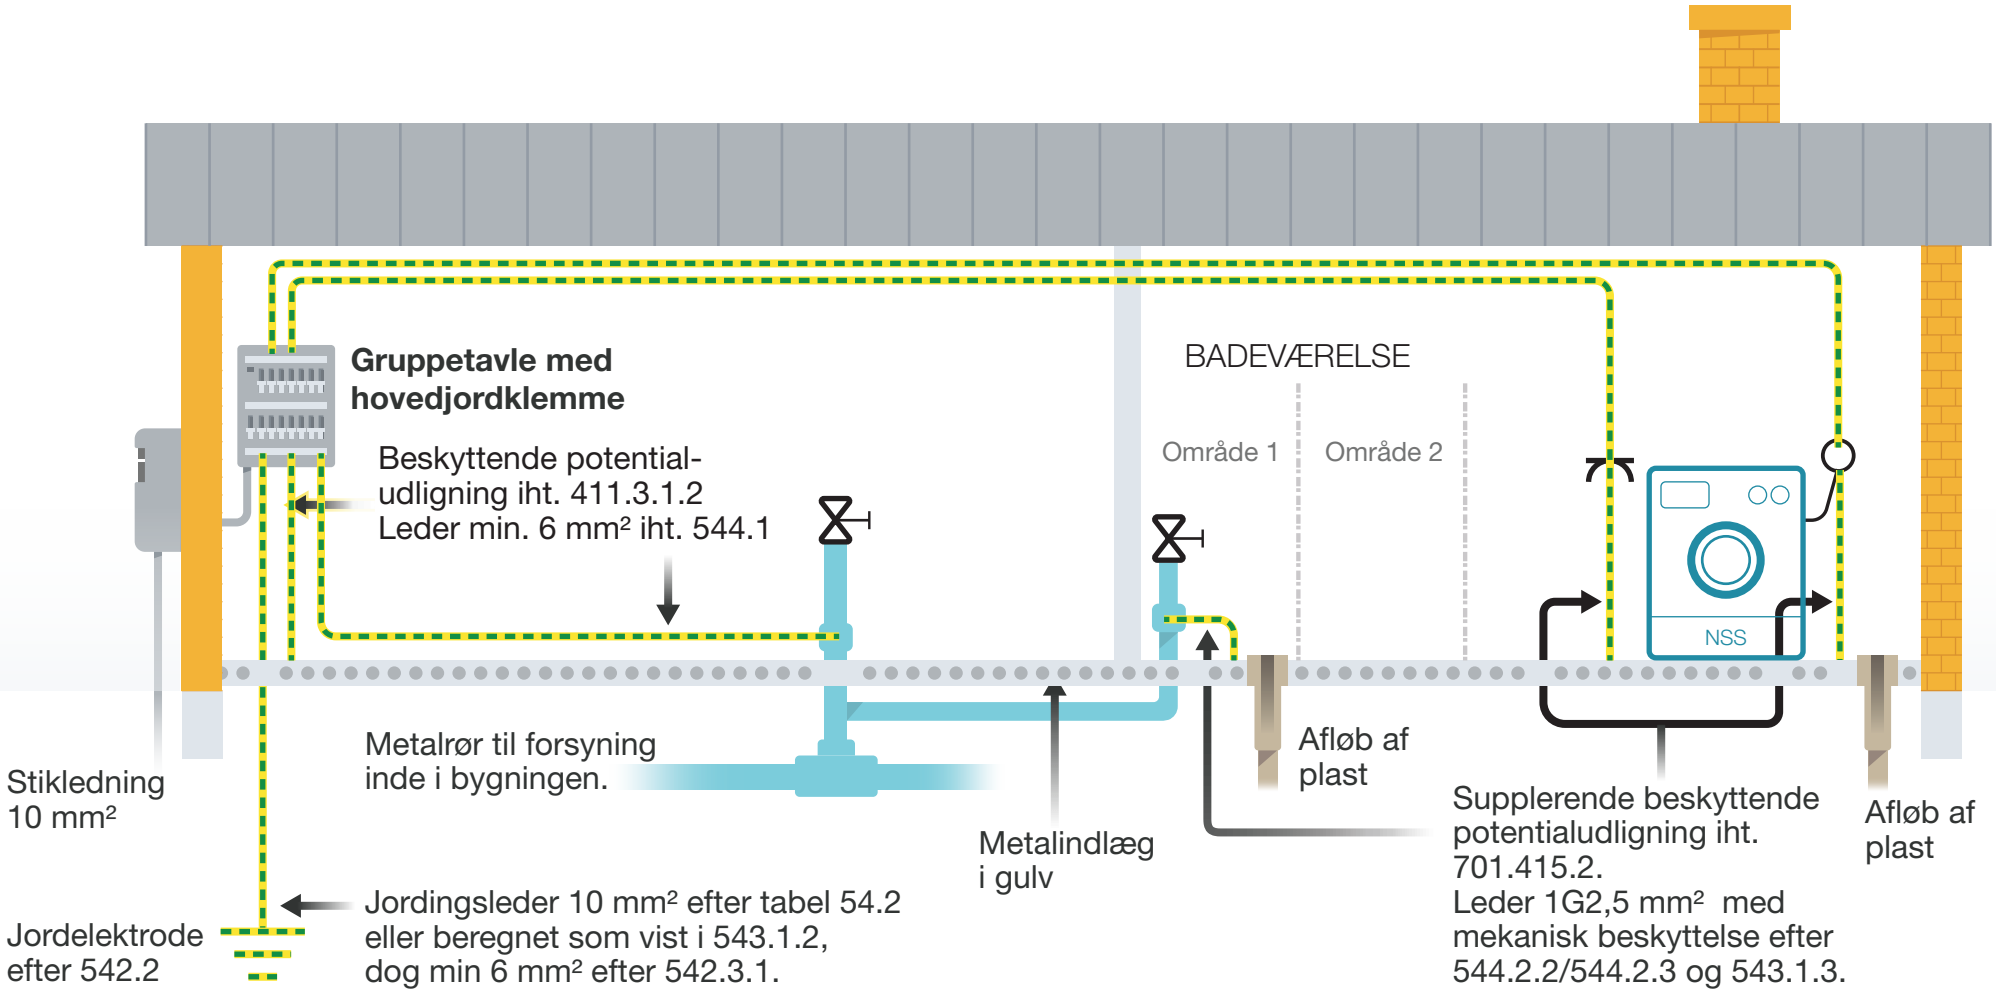


Renovering af badeværelse i bolig fra før 1994

Figur 5

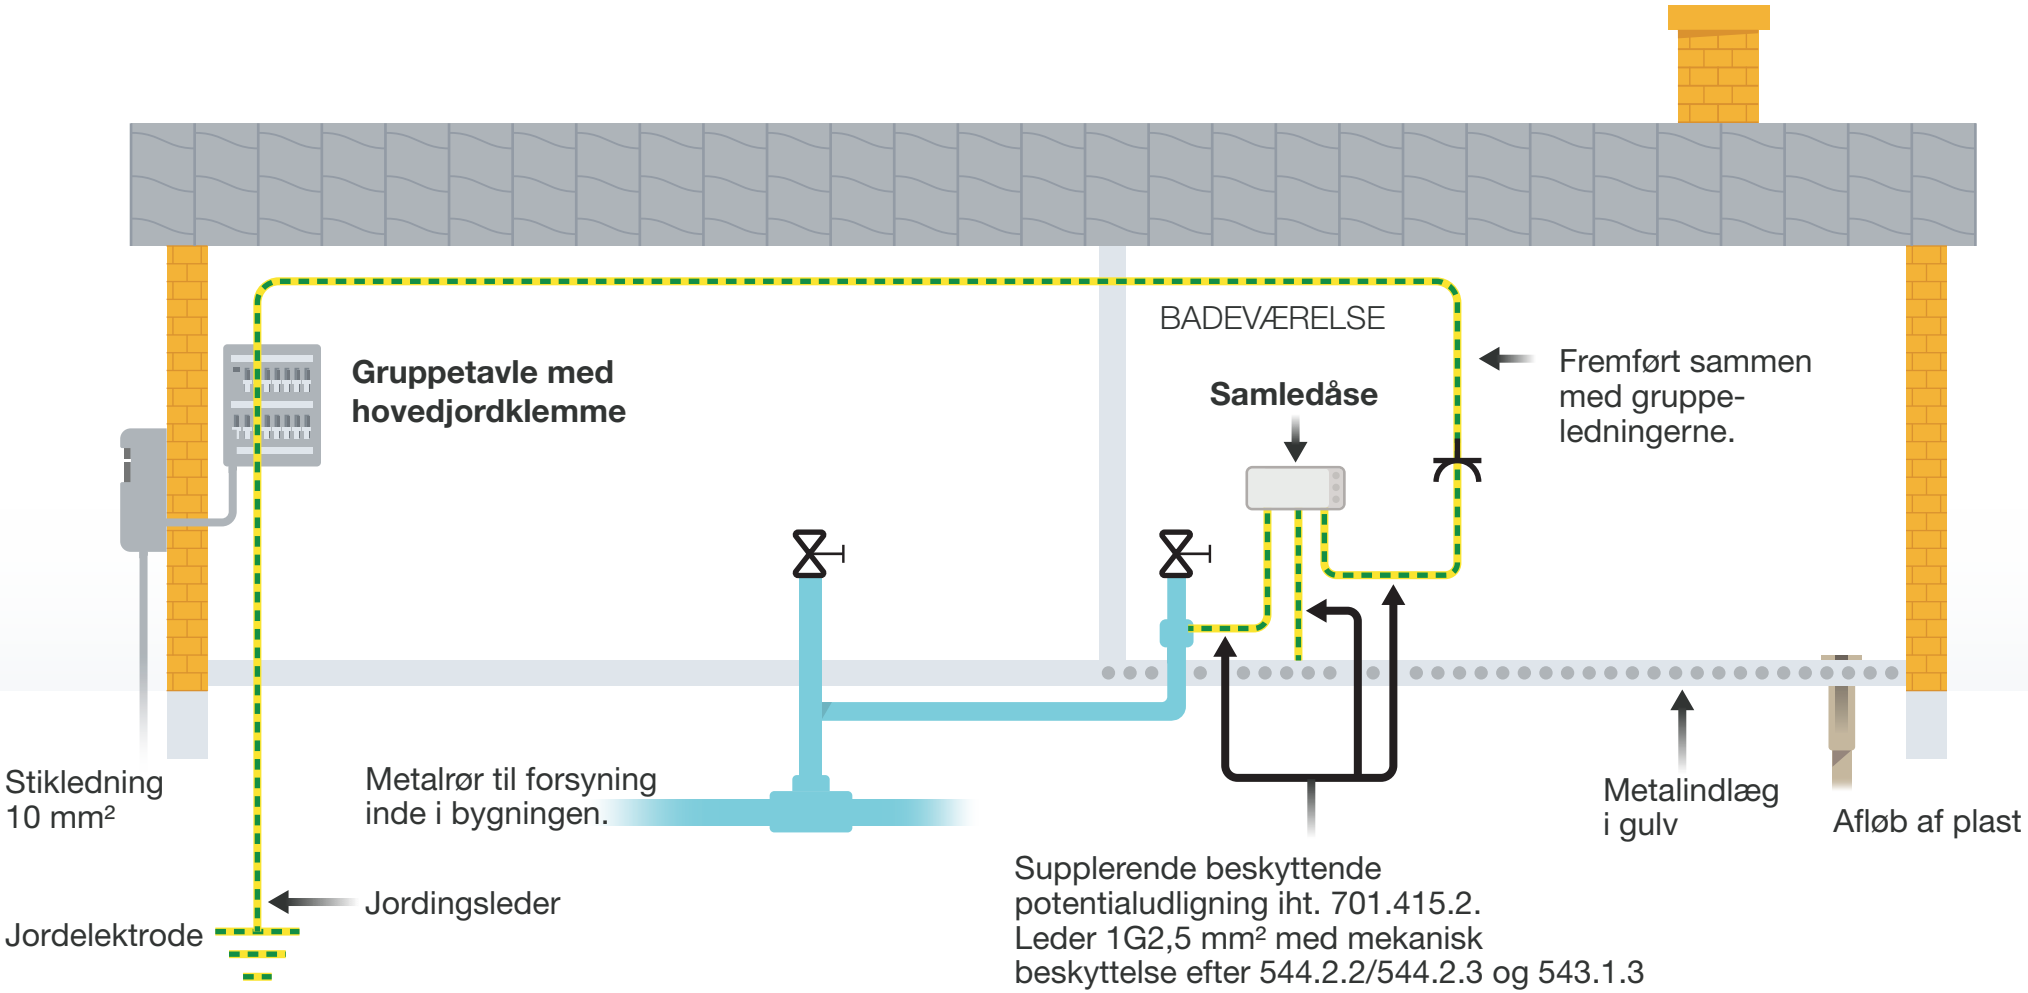


Renovering af badeværelse i en ældre bolig

Figur 6

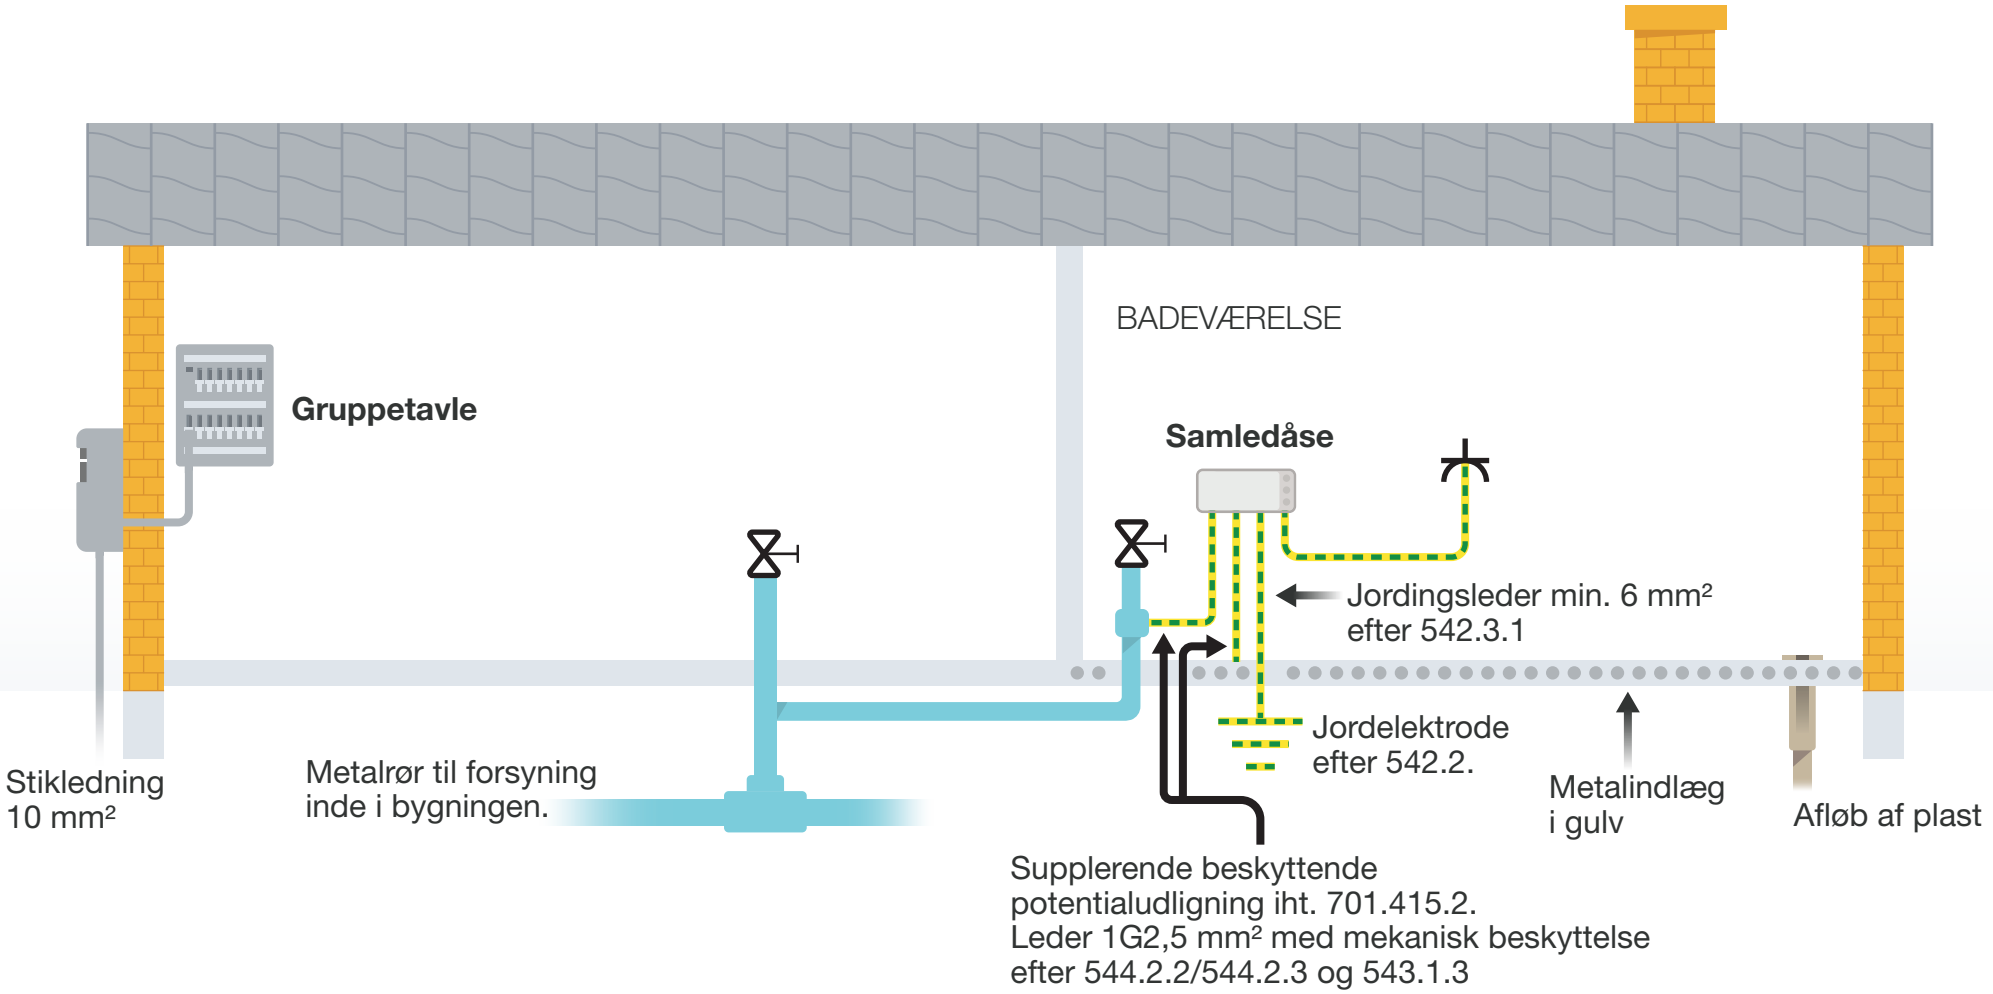


Renovering af badeværelse i bolig uden beskyttende potentialudligning

Figur 7

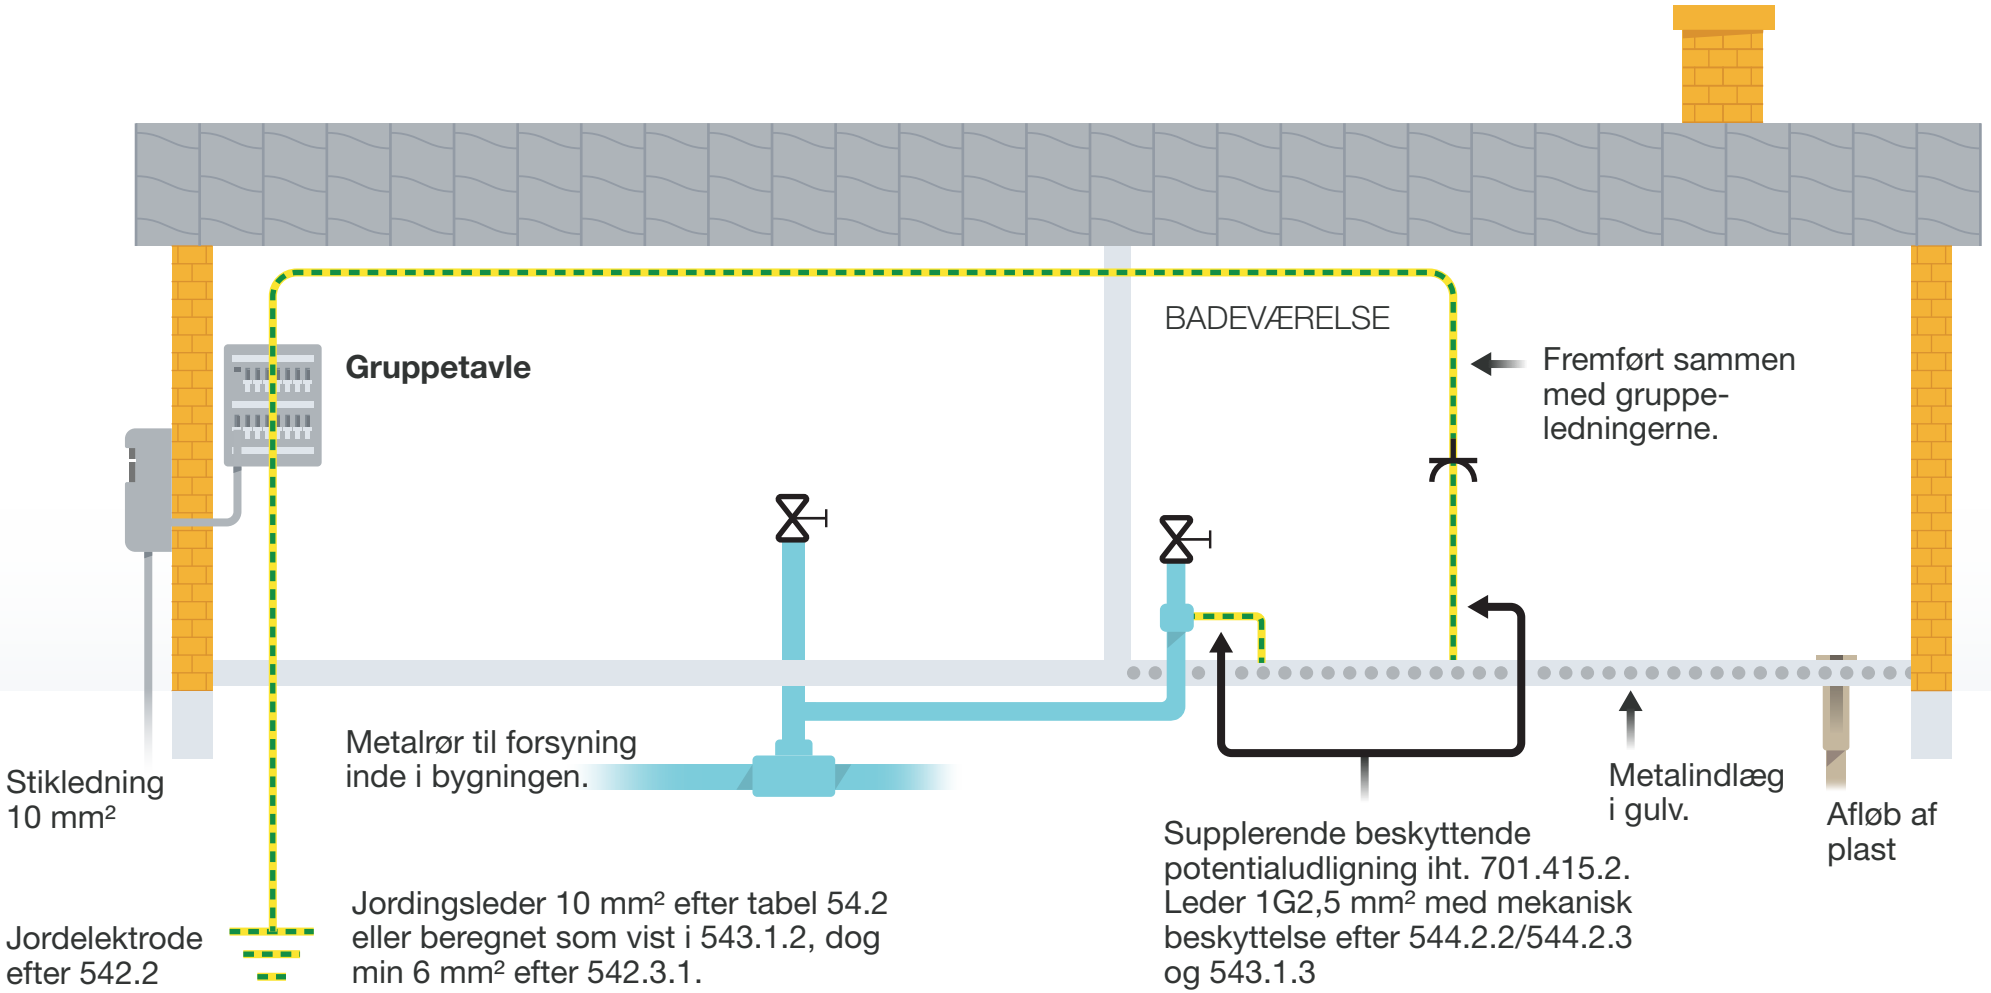


Industri med TN-system

Figur 8

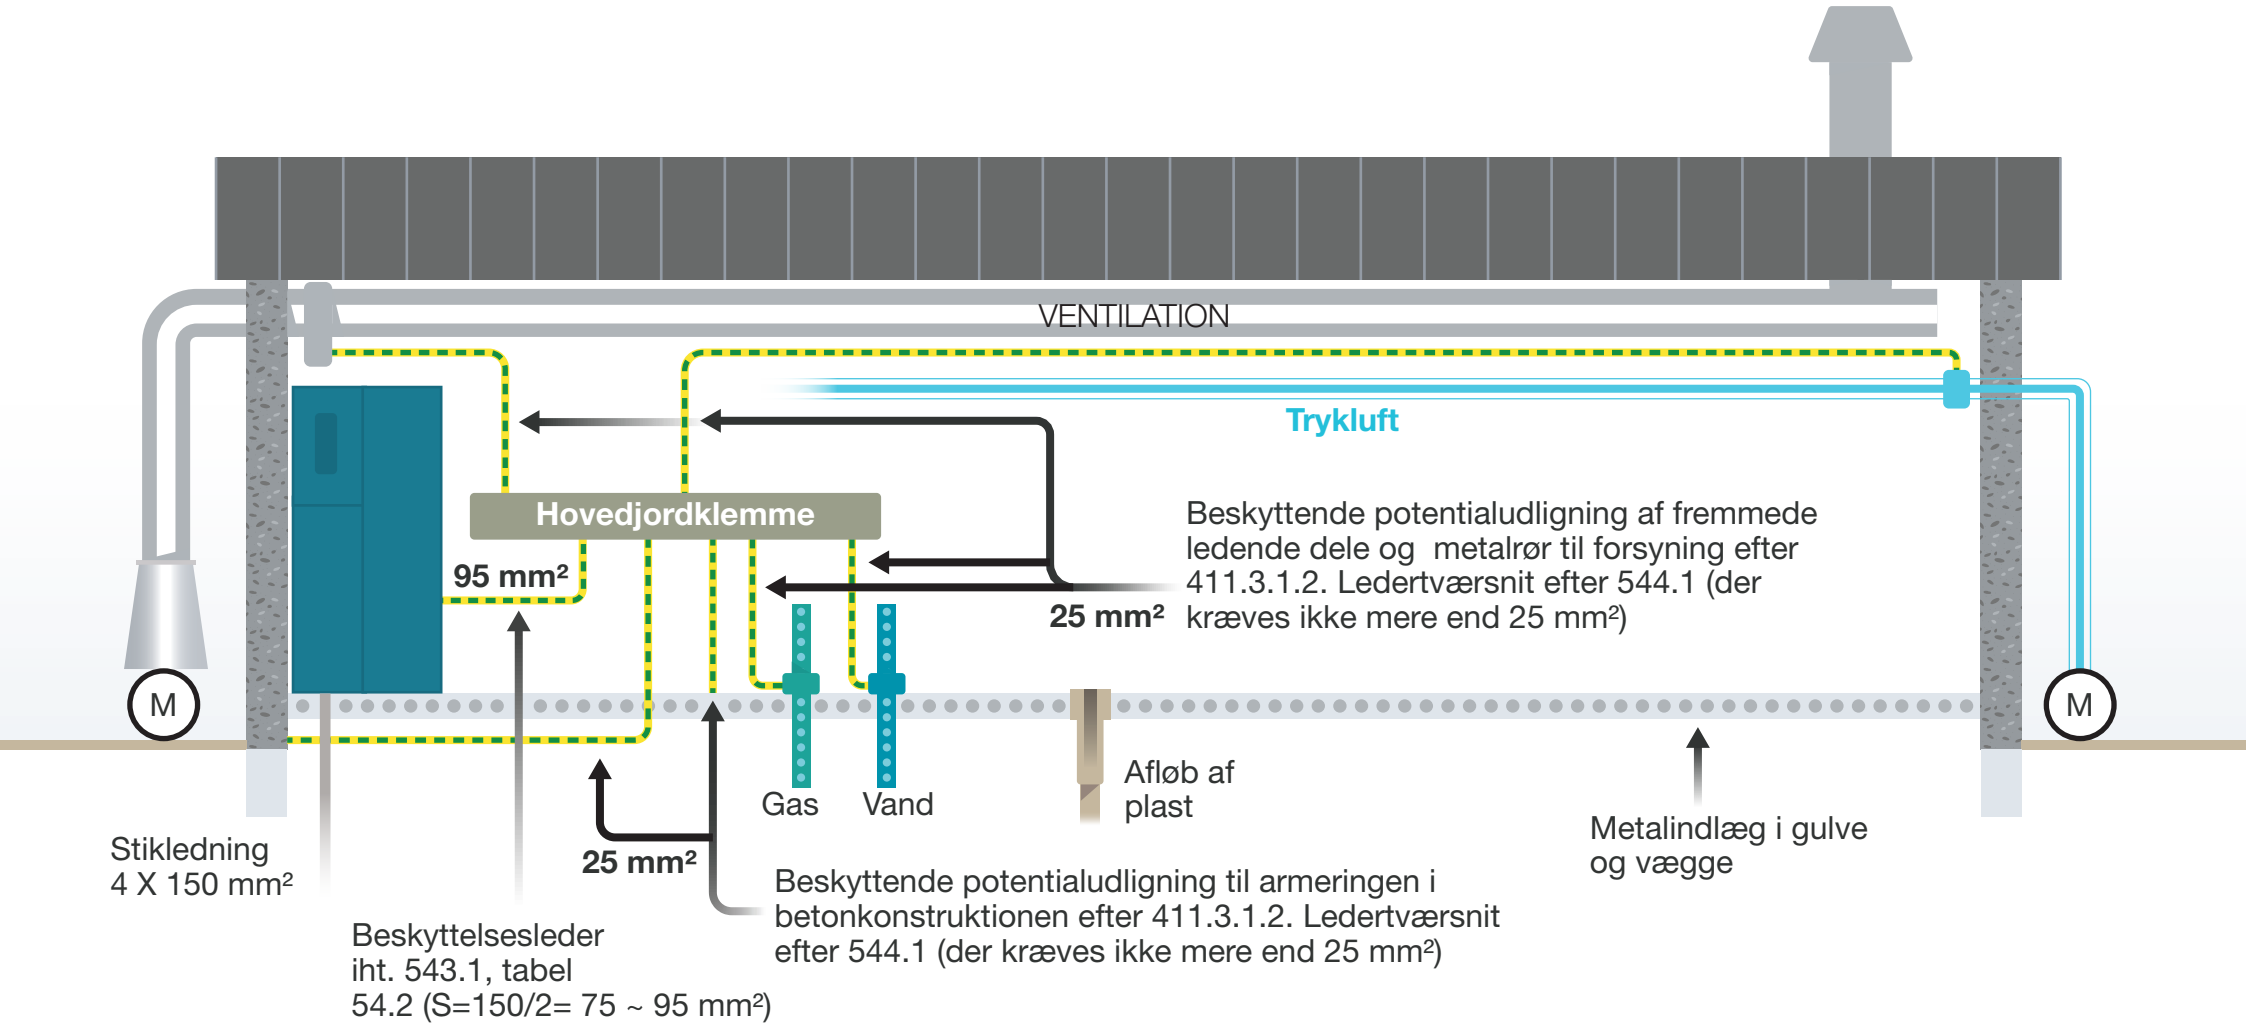

Industri med TT-system

Figur 9

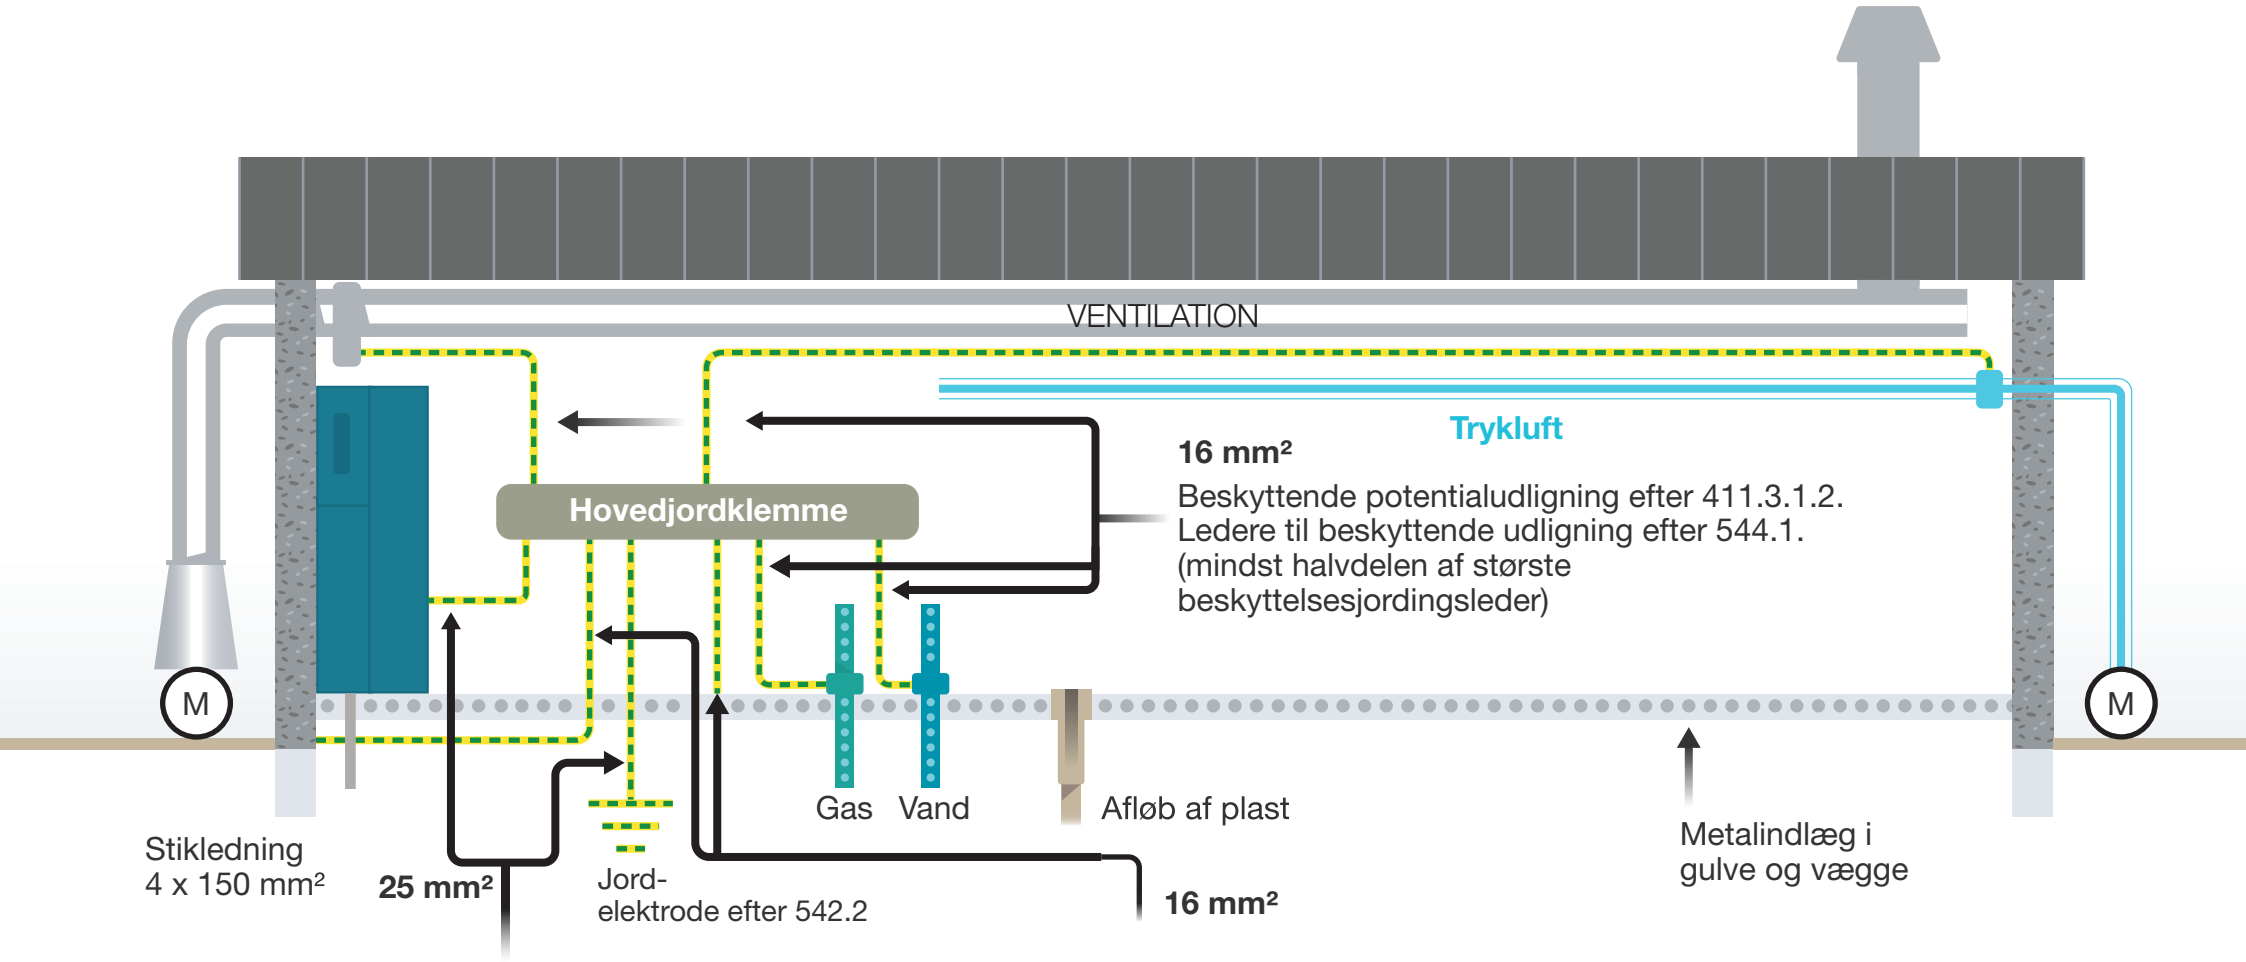

Beskyttelsesleder maks 25 mm² efter 543.1.1 eller beregnet i iht. 543.1.2. Jordingsleder maks 25 mm² efter 543.1.1 eller beregnet efter 543.1.2, dog min 6 mm² efter 542.3.1

Beskyttende potentialudligning til metalarmeringen i bygningsdele iht. 411.3.1.2. Ledere til beskyttende udligning efter 544.1